


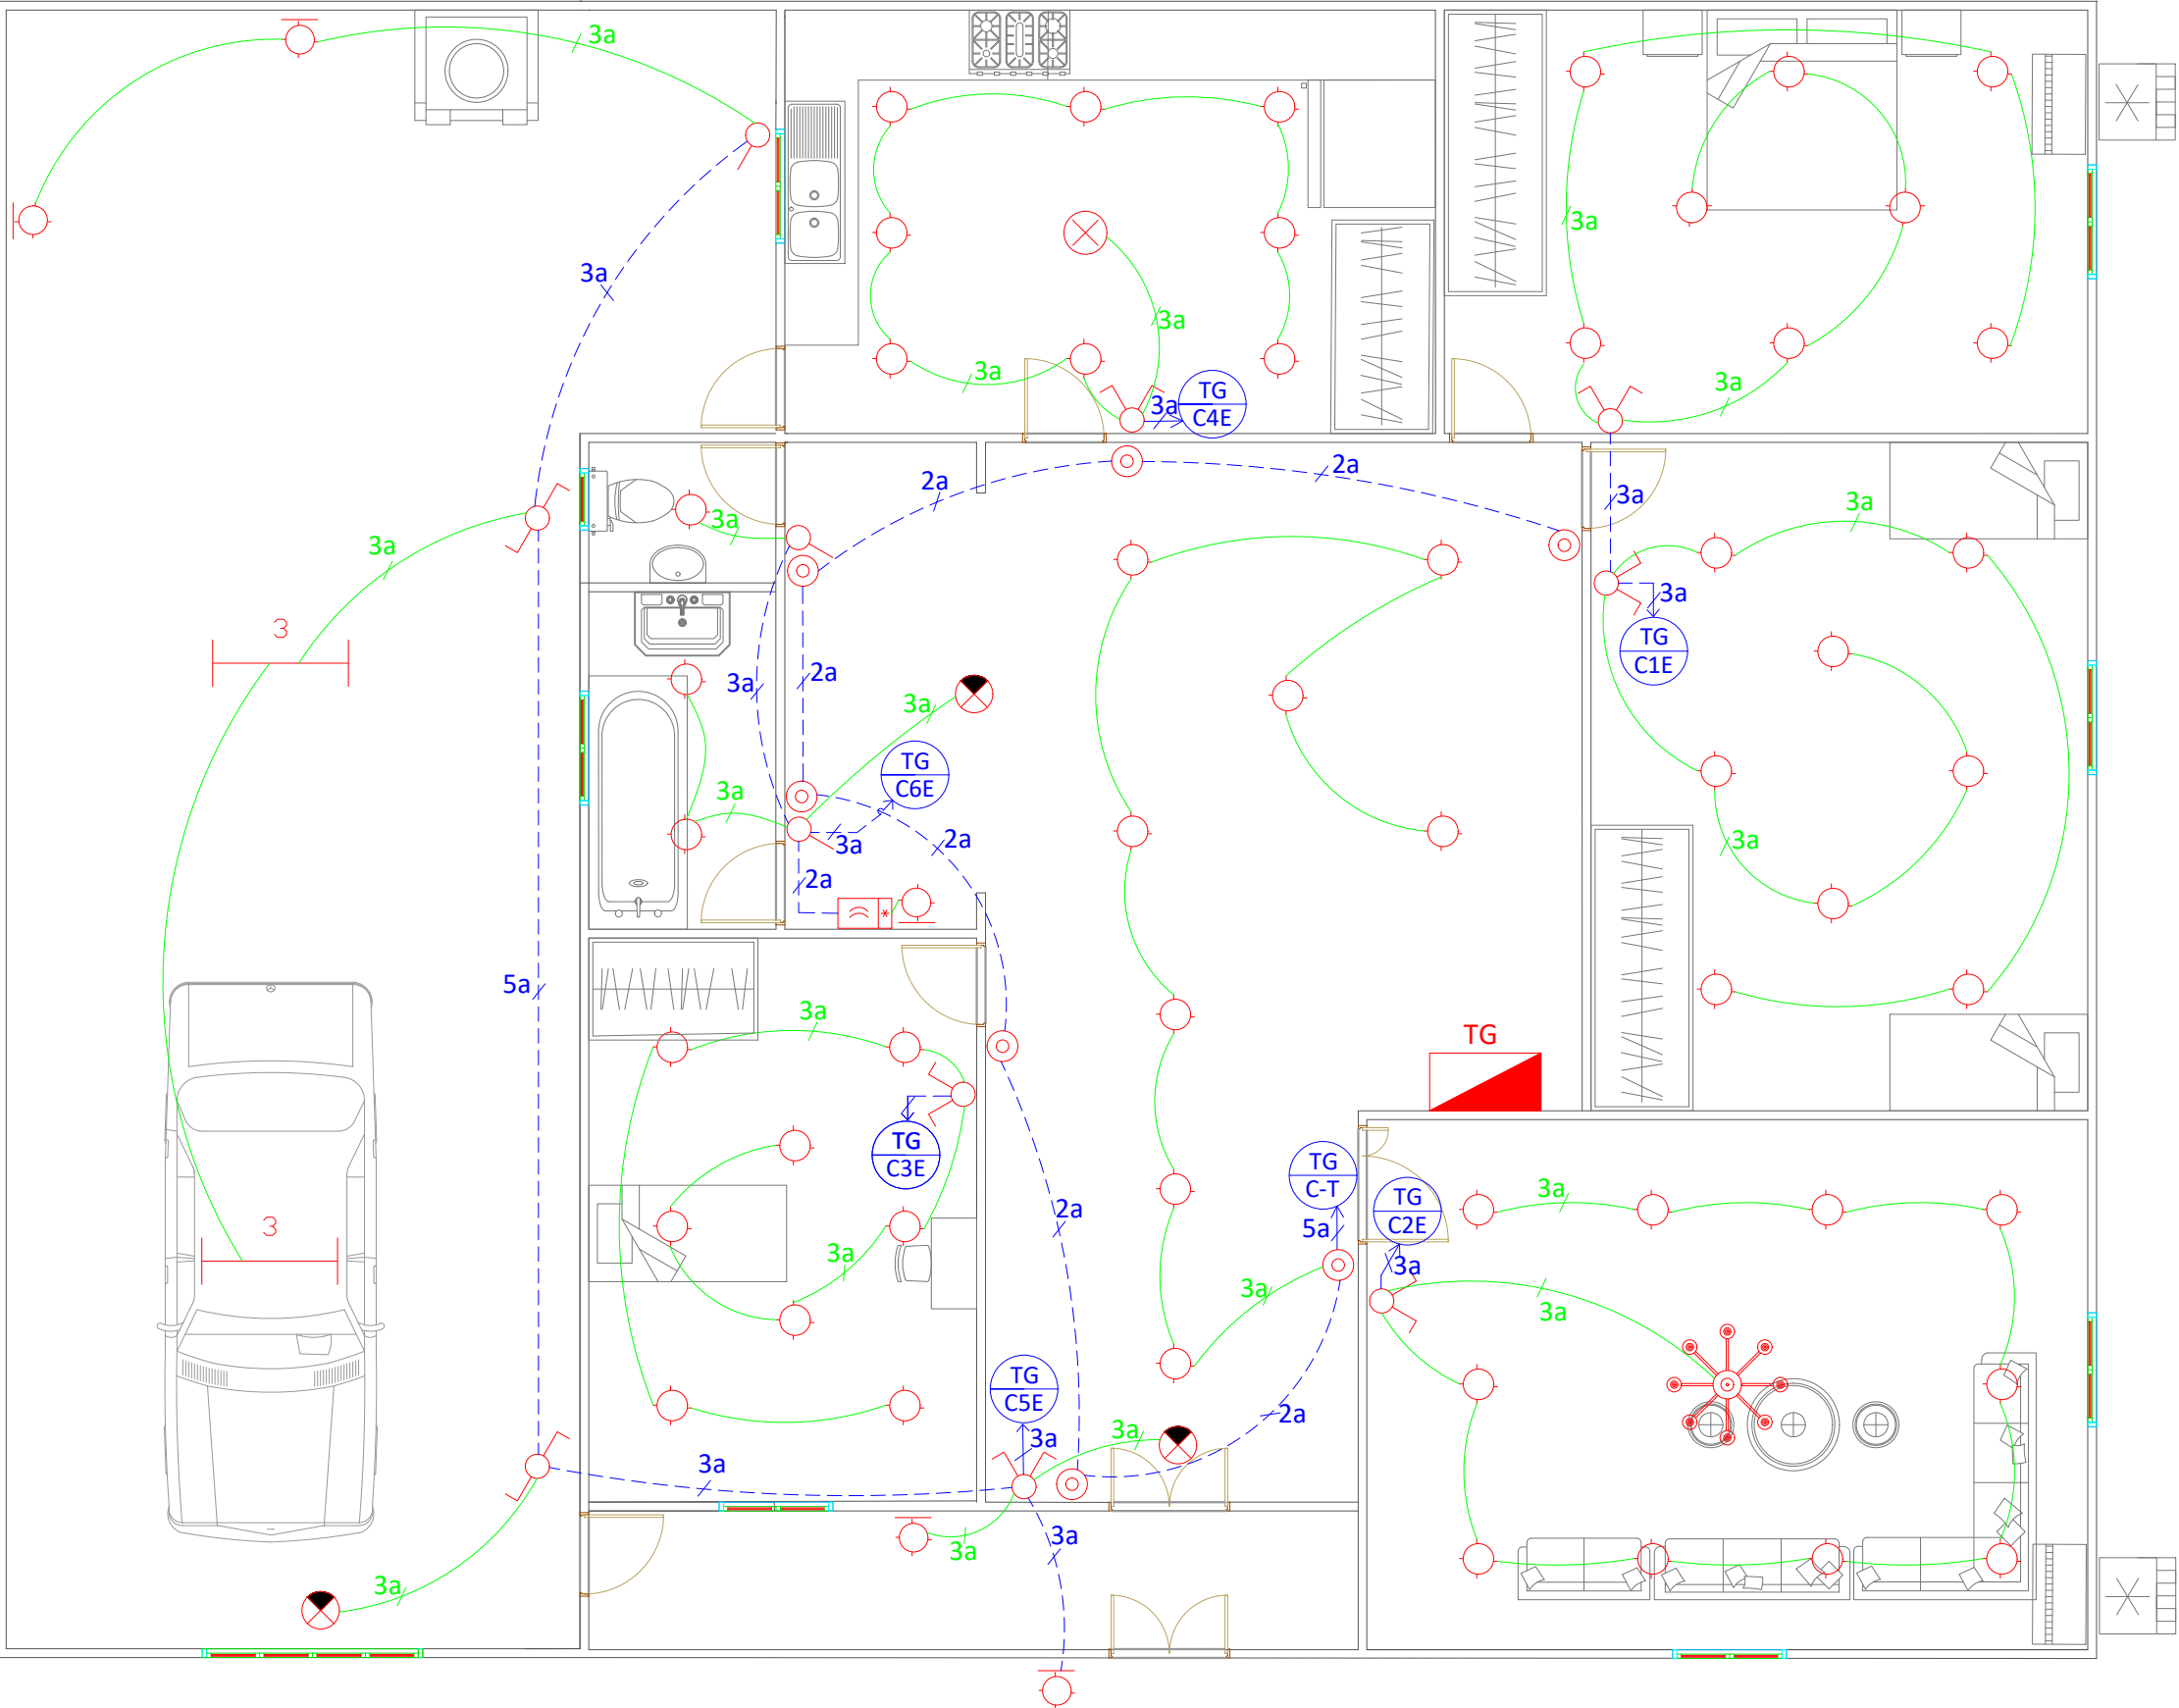

Légende	
	Spot LED
	Applique murale
	Luminaire MultiLampe
	3 Tube Néon LED
	Lampe d'éclairage de sécurité
	Interrupteur simple Allumage , hauteur du sol : 120cm
	Interrupteur double Allumage , hauteur du sol : 120cm
	Interrupteur va et vient , hauteur du sol : 120cm
	Bouton poussoir , hauteur du sol : 120cm
	Detecteur de présence
	Tableau général (TG)
	Circuit n: 1 d'Éclairage vers Tableau Général
	Circuit Télérupteur vers Tableau Général
X a	X : nombre de conducteur de section: 1.5 mm²
	Canalisation entre toit et faux plafond ET/OU en mur
	Canalisation souterraine ET/OU en mur