


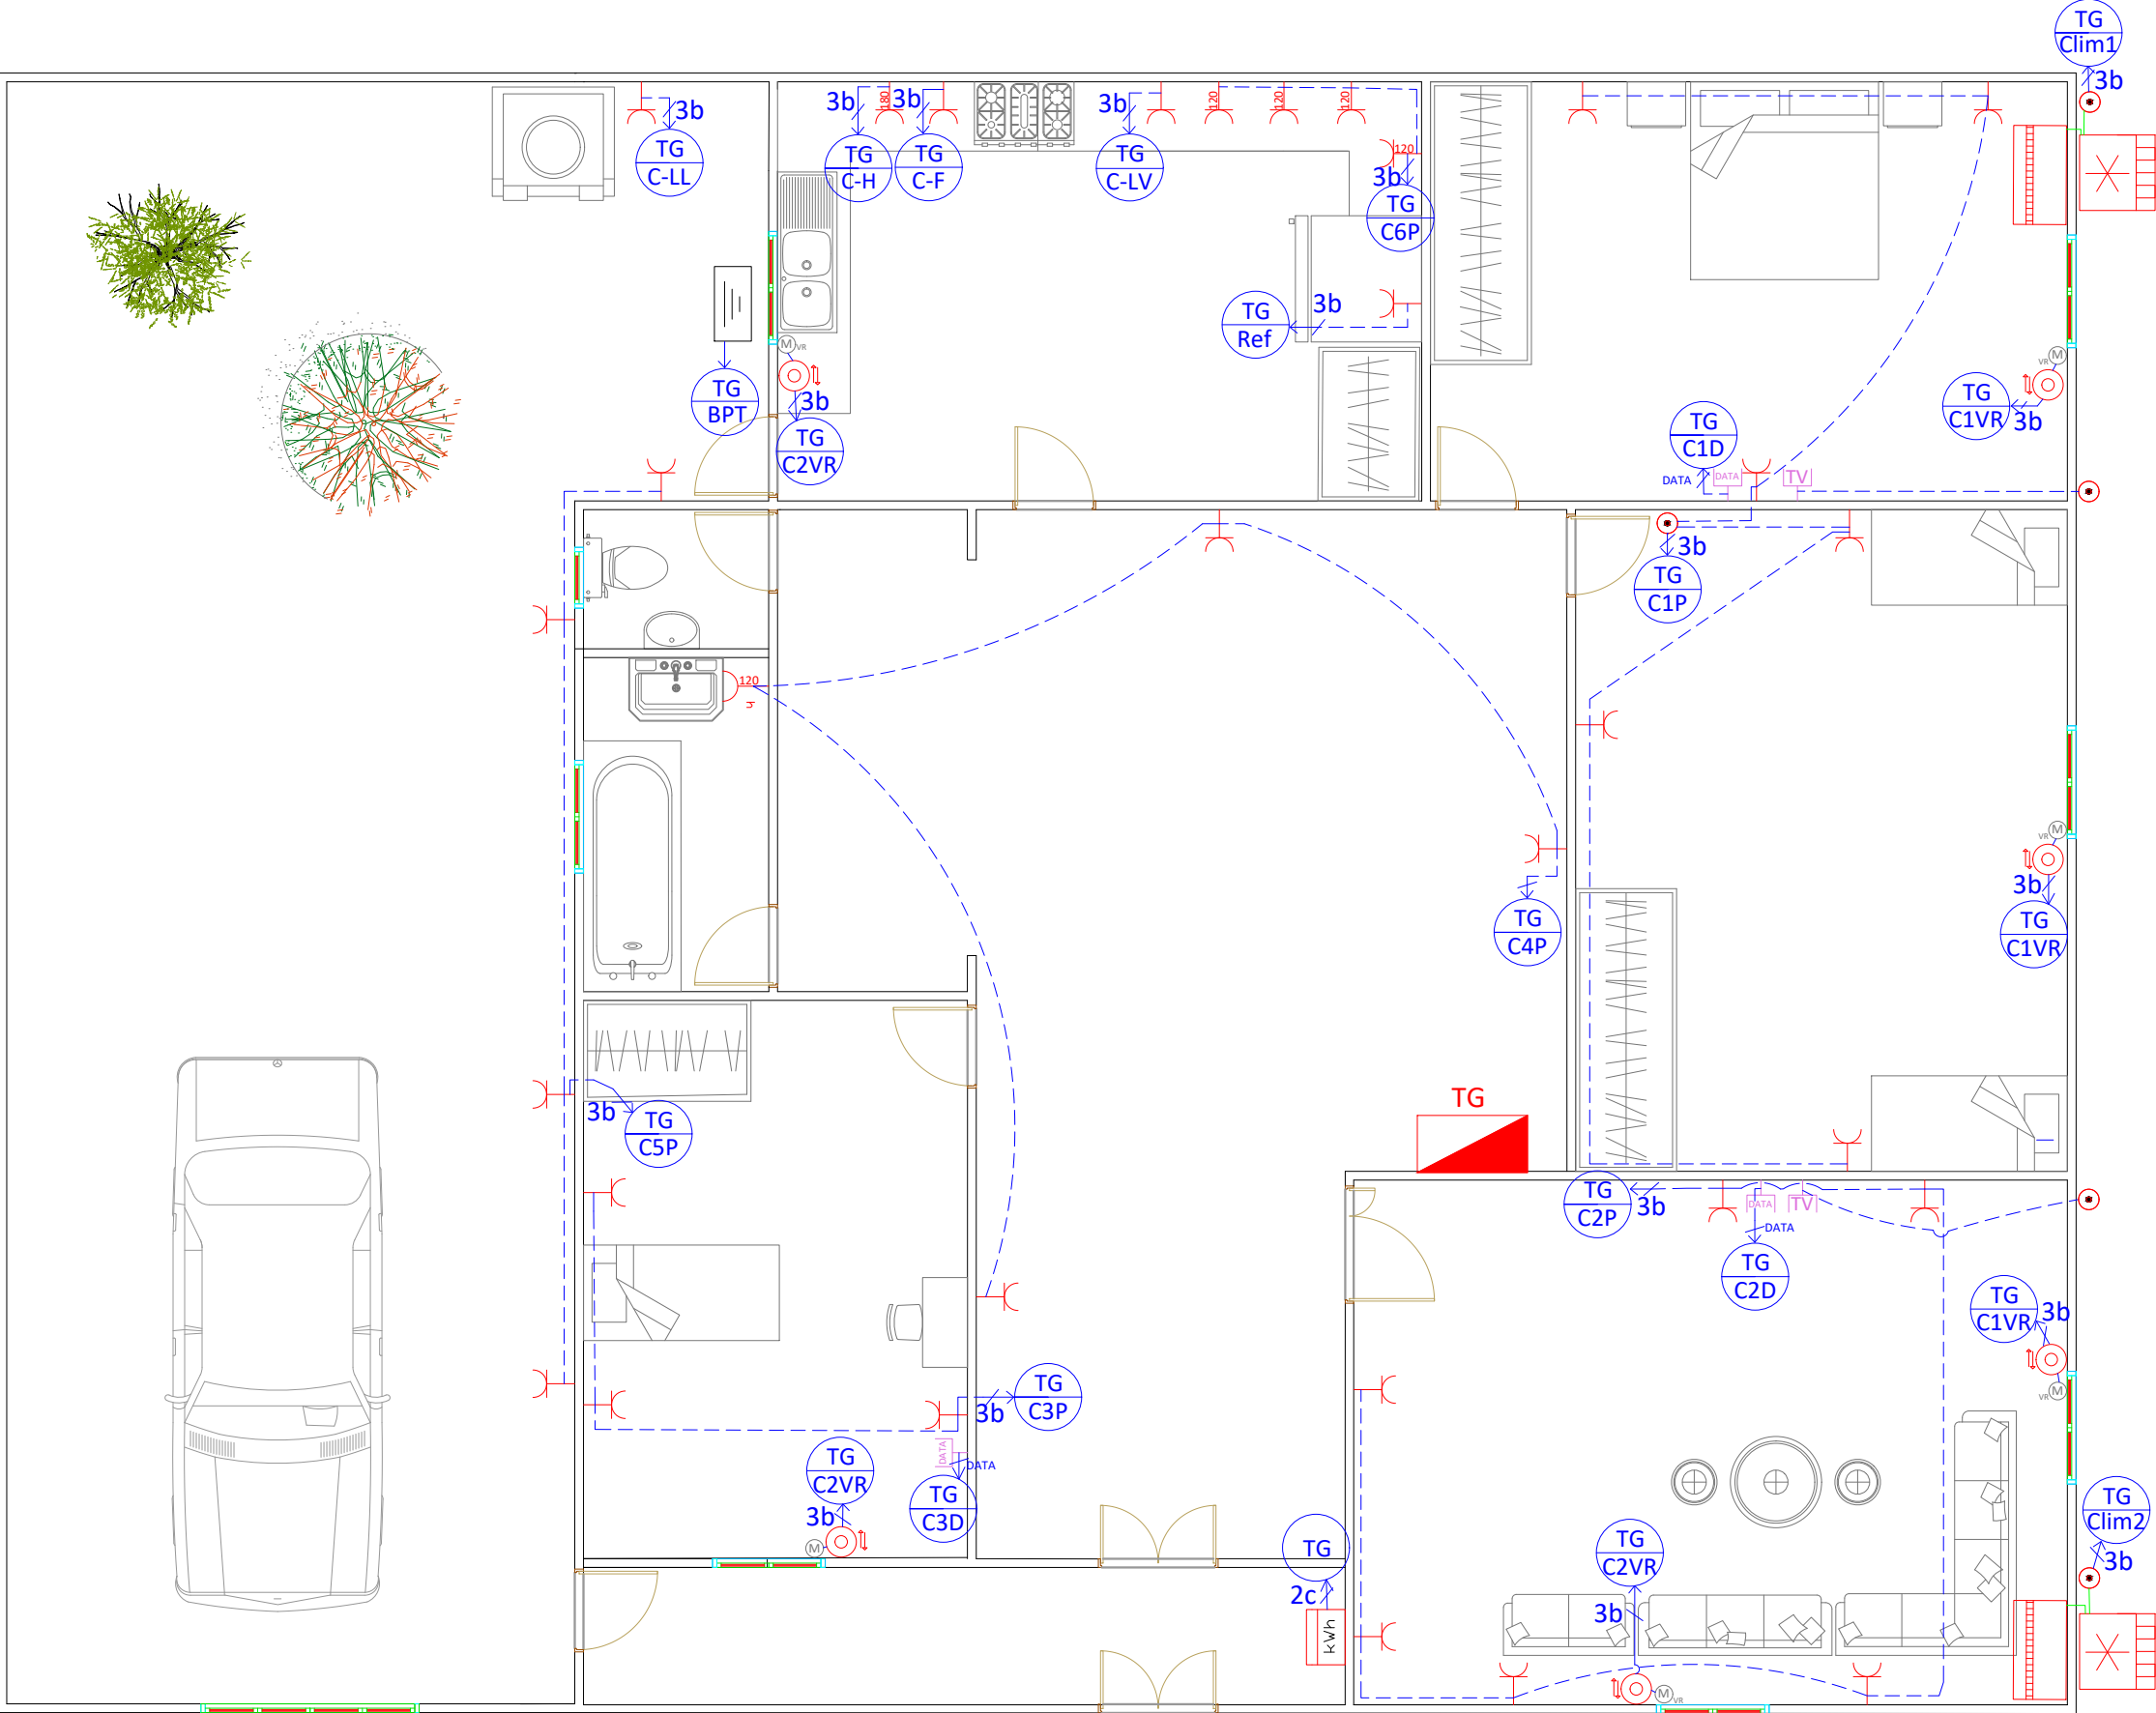

Légende	
	prise de courant 2P+T ,hauteur du sol : 45cm
	prise de courant étanche ,hauteur du sol : 120cm
	prise de télévision
	prise de communication RJ45
	Bouton poussoir 2 direction
	Boîte de dérivation
	Tableau général (TG)
	Circuit n: 1 de prise vers Tableau Général
	Circuit n: 1 de Voulets roulant vers Tableau Général
	Circuit n: 1 de cable de Données vers Tableau Général
	Circuit Climatiseur n: 1 ; vers Tableau Général
	Circuit de Four, Hotte, Lave vaisselle ; vers Tableau Général
	Circuit de Réfrigérateur, Lave Linge ; vers Tableau Général
X a,b,c ; DATA	X : nombre de conducteur de section: 1.5, 2.5 , 10 (mm²); Cable de données
	Compteur d'énergie électrique (kWh)
	Canalisation souterraine ET/OU en mur